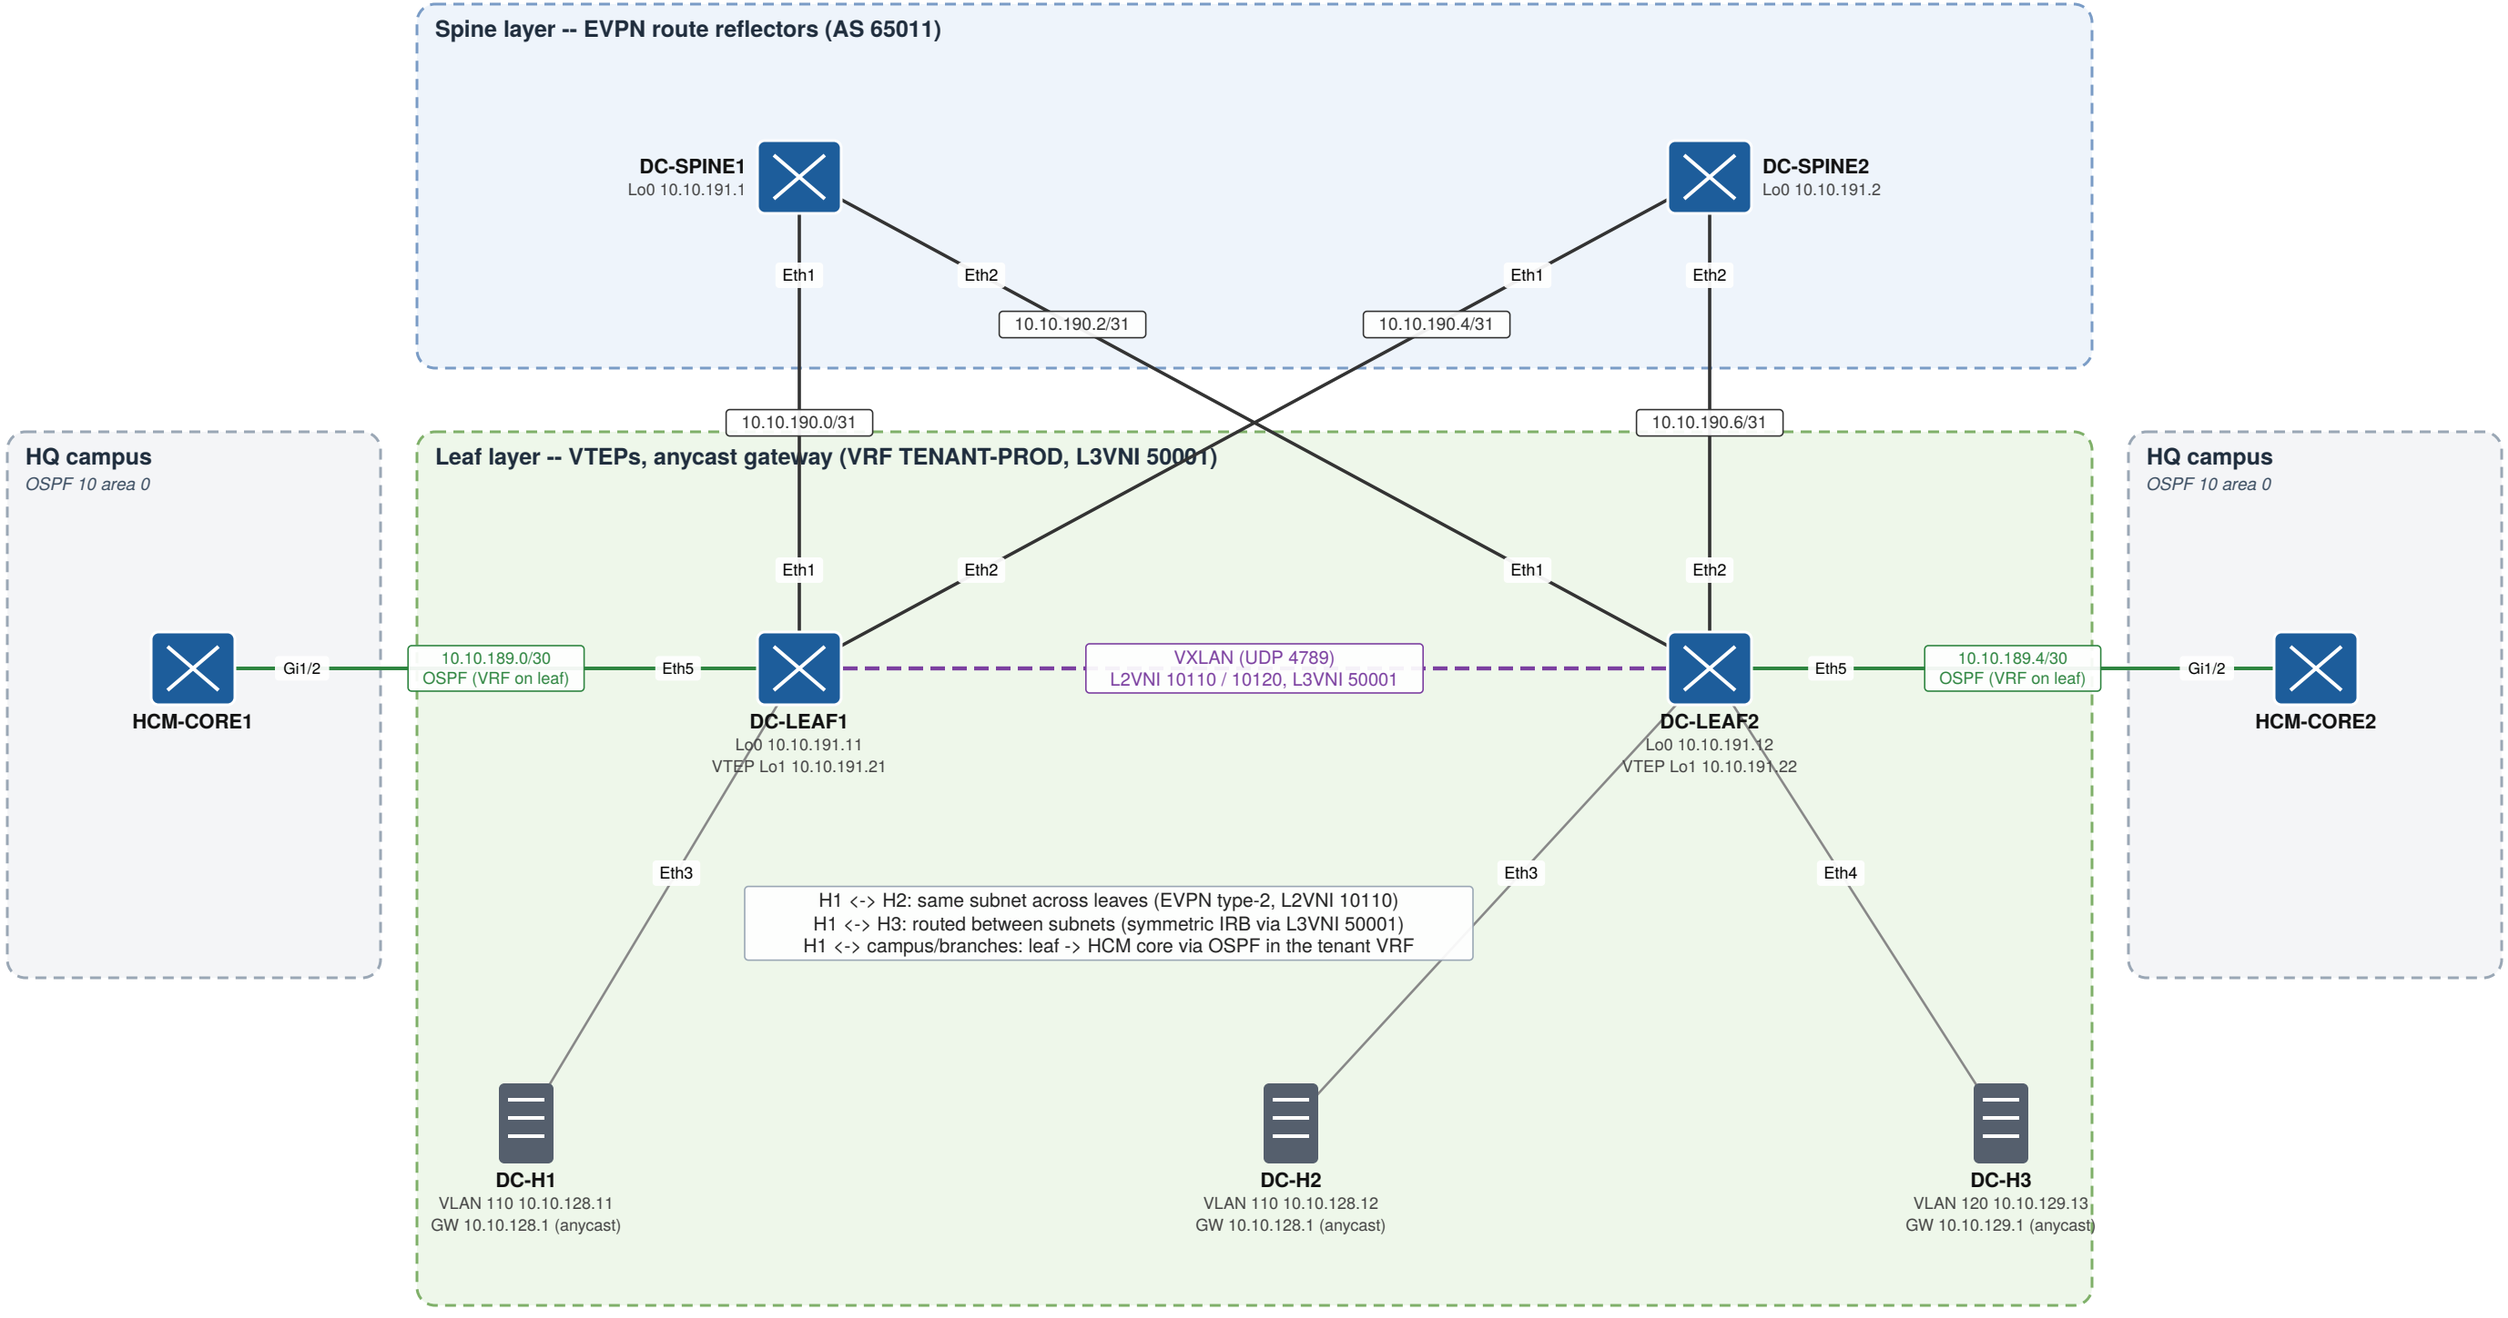HQ data-centre fabric: OSPF underlay, iBGP EVPN overlay, VXLAN data plane, border to the campus core